



VÍAS METROPOLITANAS


SECCIÓN VÍAL 1-1: VIA ARTERIAL
AV. EJÉRCITO TRAMO CAYMA

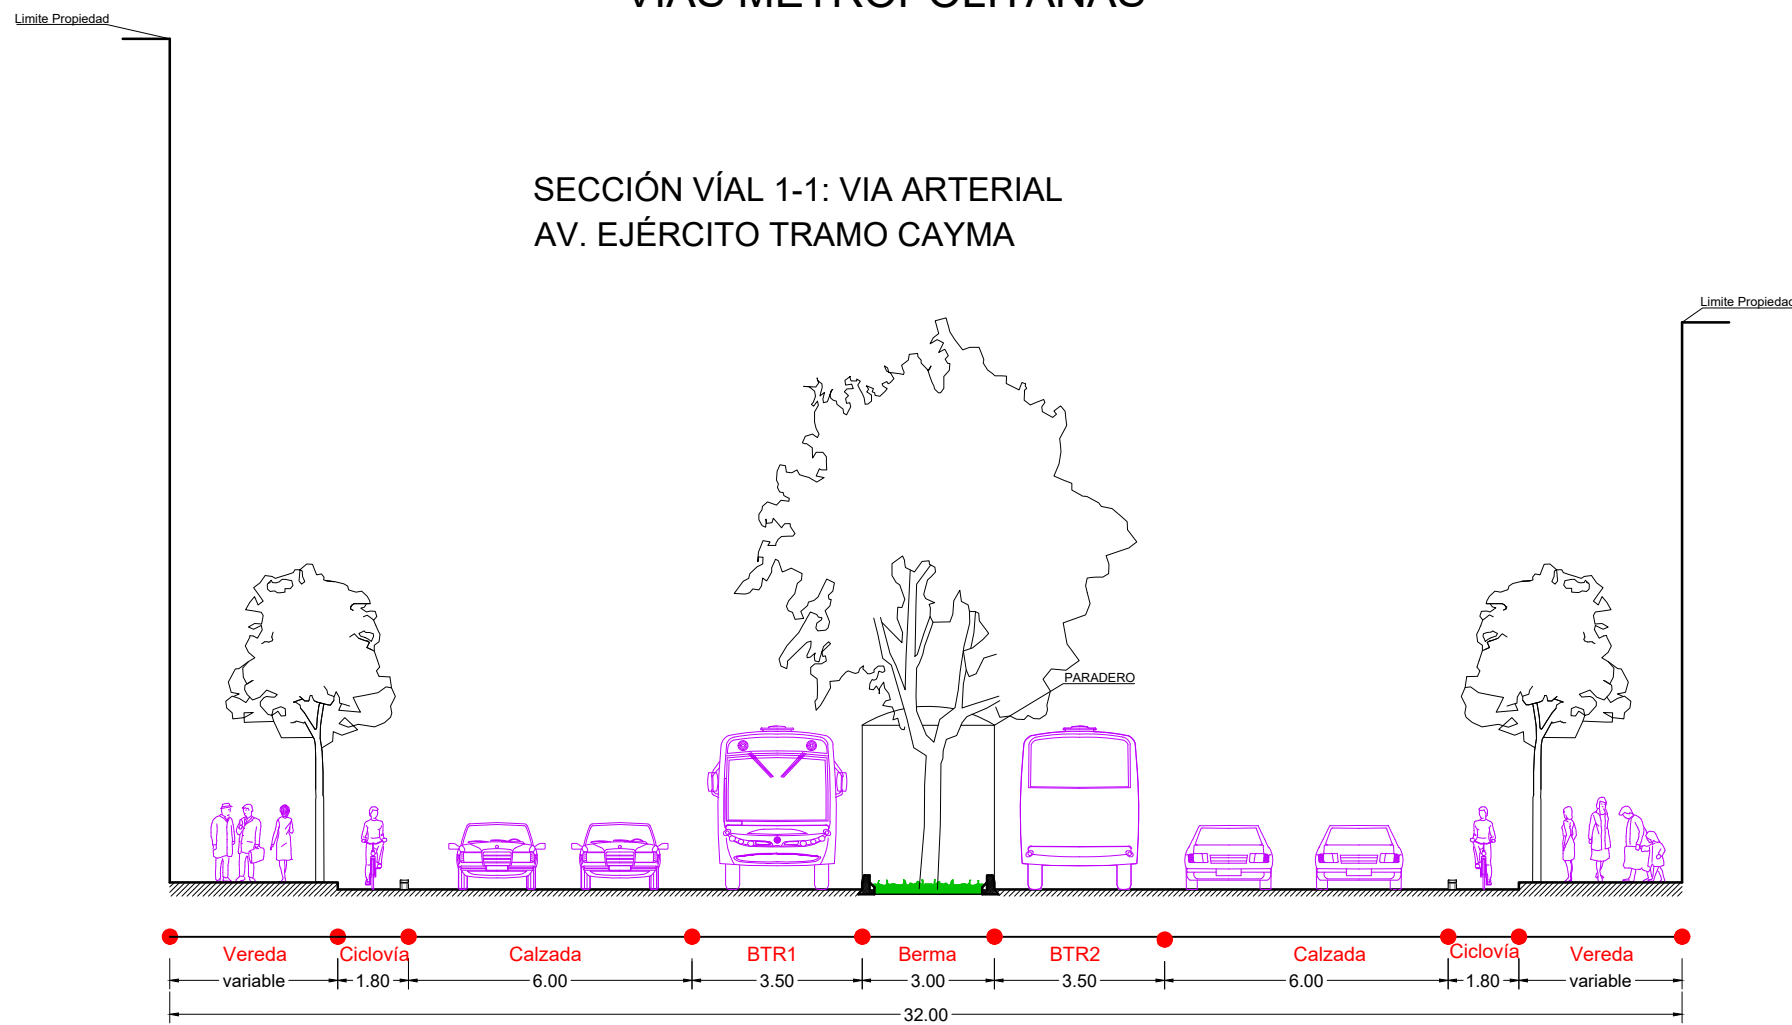


SECCIÓN VÍAL 2-2: VIA ARTERIAL
AV. EJÉRCITO TRAMO YANAHUARA

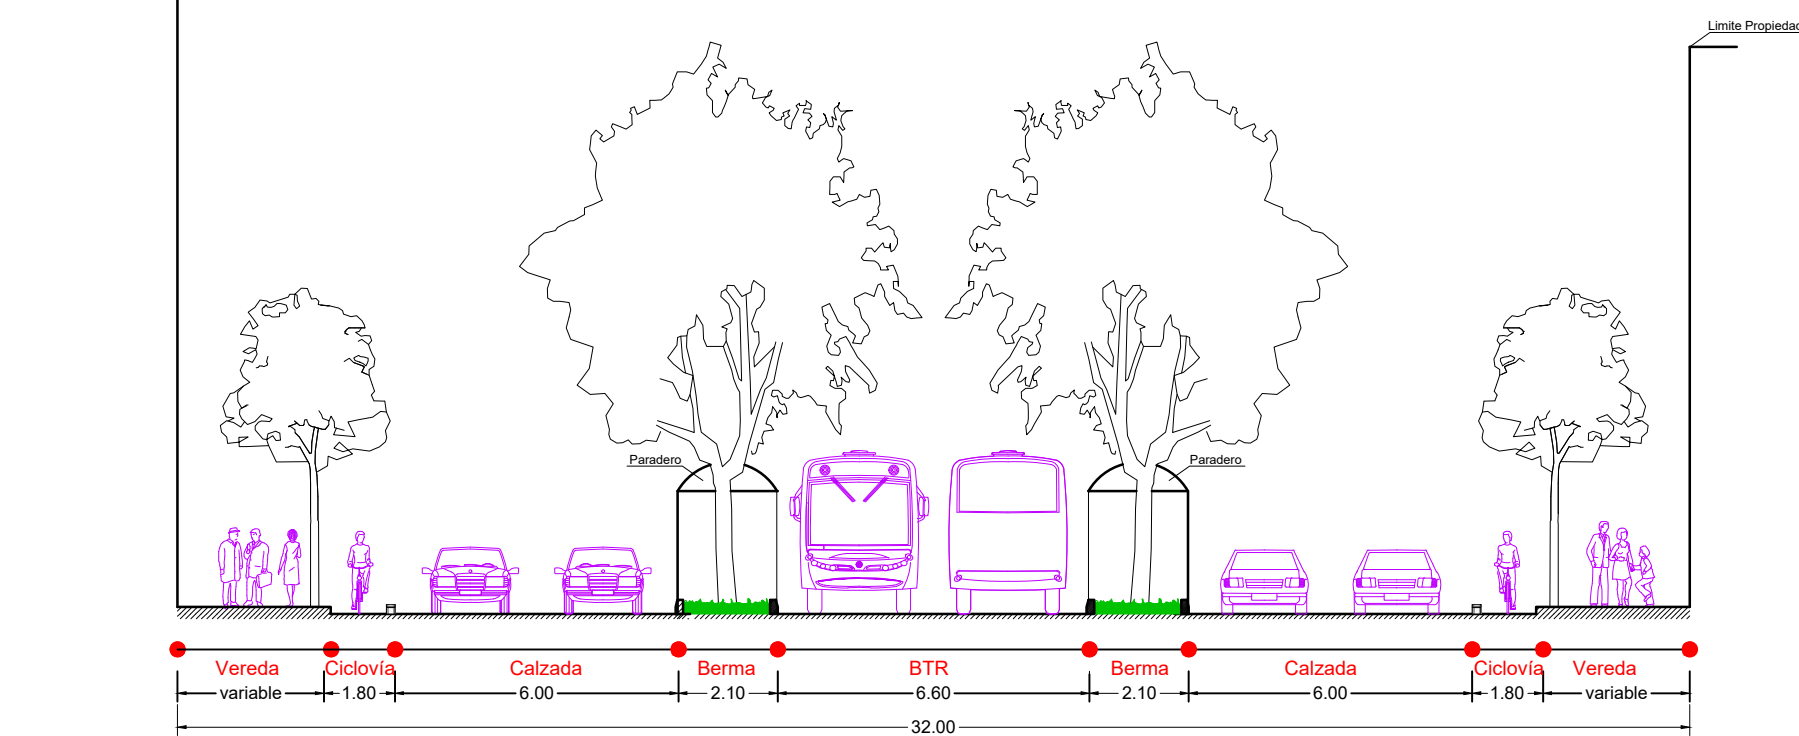


SECCIÓN VÍAL 3-3: VIA ARTERIAL
AV. PARRA

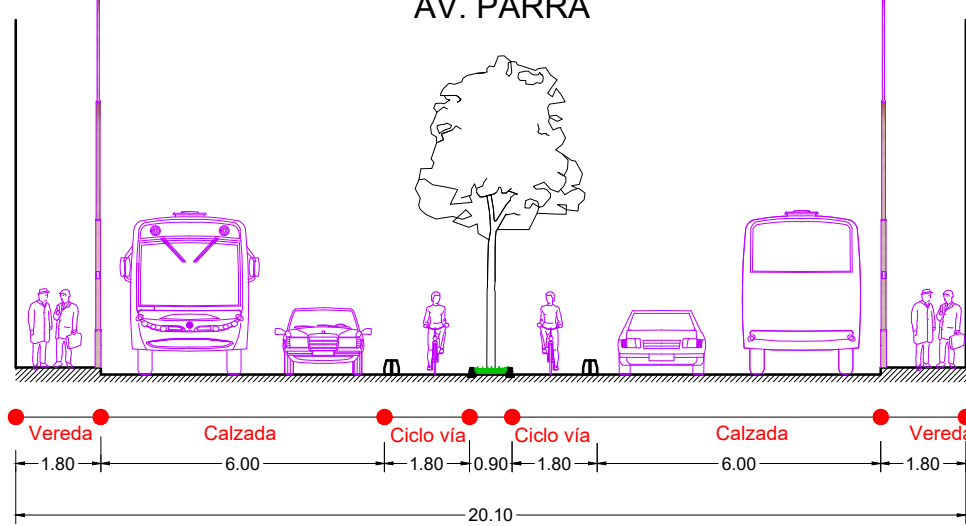


SECCIÓN VÍAL 4-4: ANILLO VIAL
AV. JUAN DE LA TORRE
TRAMO UCSP

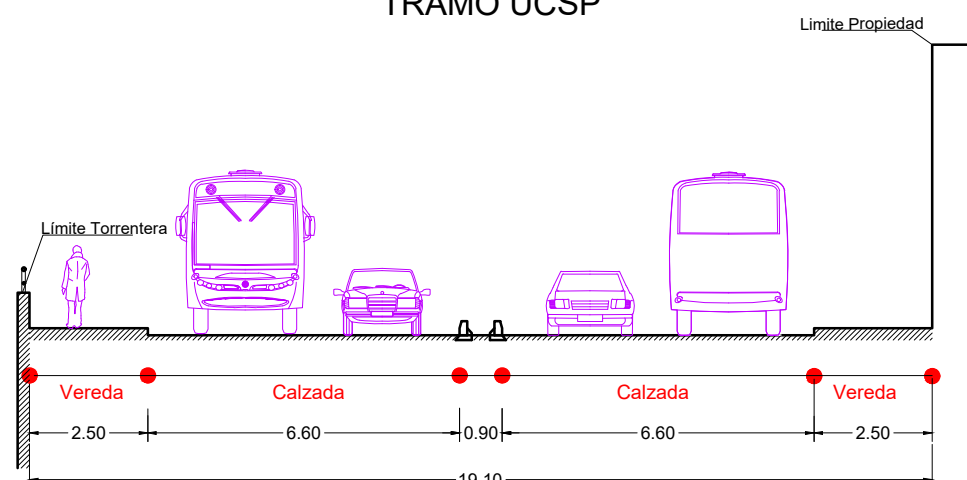

SECCIÓN VÍAL 5-5: ANILLO VIAL
AV. JUANE LA TORRE
TRAMO PARQUE GRAU

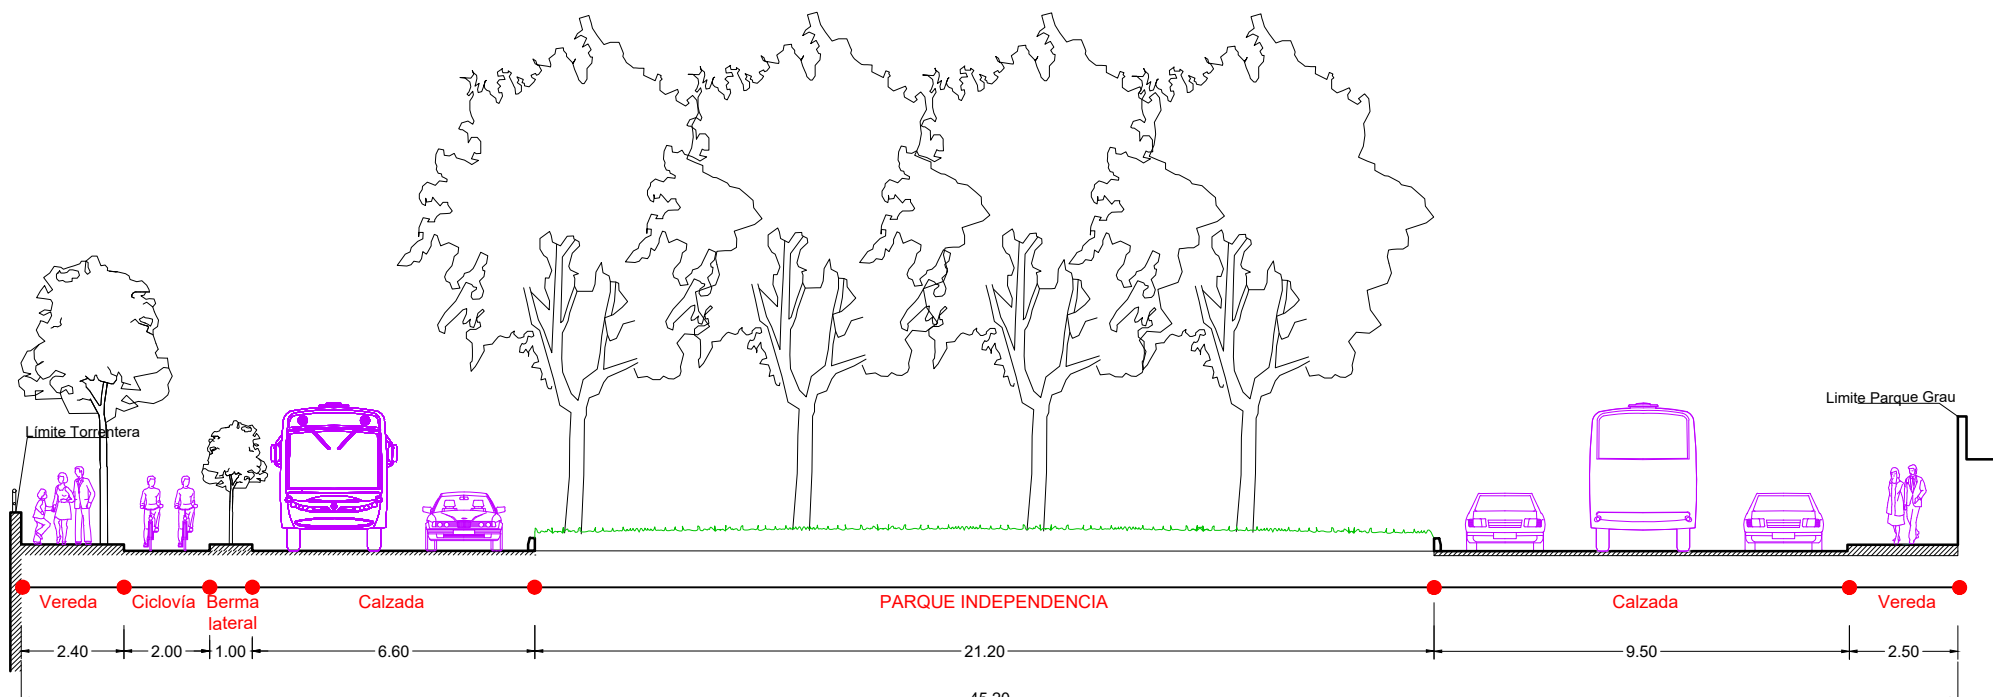

SECCIÓN VÍAL 6-6: ANILLO VIAL
AV. LA MARINA
TRAMO PUENTE GRAU

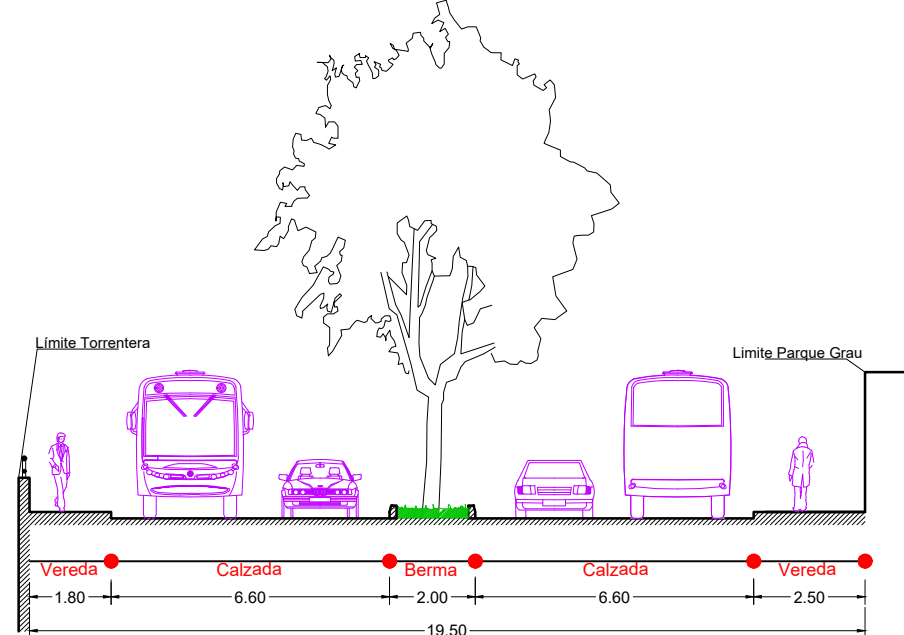

MUNICIPALIDAD PROVINCIAL
DE AREQUIPA

IMPLA
Instituto Municipal
de Planeamiento



GERENCIA DEL CENTRO HISTÓRICO
Y ZONA MONUMENTAL
ÁREA DE PLANIFICACIÓN
Y GESTIÓN URBANA



AECID
AGENCIA ESPAÑOLA
DE COOPERACIÓN INTERNACIONAL
PARA EL DESARROLLO

**Plan Maestro del Centro
Histórico de Arequipa y
Zona de Amortiguamiento
PlaMCha
2025-2035
PF.04**

PLANO

**PROPUESTA VIAL
SECCIONES VIALES 1**

ESC 1/4 500 NOVIEMBRE 2025 PSAD 56

MUNICIPALIDAD PROVINCIAL DE AREQUIPA

Alcalde
Ing. VICTOR HUGO RIVERA CHÁVEZ

IMPLA
Gerente General
Arq. PATRICIA MUÑOZ MEDINA

GERENCIA DEL CENTRO HISTÓRICO Y
ZONA MONUMENTAL

Gerente
Arq. GABRIEL RAMIRO DAMIANI LAZO

Coordinador Técnico General
Arq. JULIO C. ASPILCUETA BARBACHÁN

Equipo Técnico
Arq. Nancy Benavente Valcárcel
Arq. Yrma Daniela Villalba Linares
Arq. Candy Vanessa Año Urquiza
B.Arq. Rodrigo Arrieta Buscaglia
Abog. Juana Janina Tiznado Yana