




SECCIÓN VÍAL 7-7: ANILLO VIAL
AV.LA MARINA TRAMO QUINTA SALAS

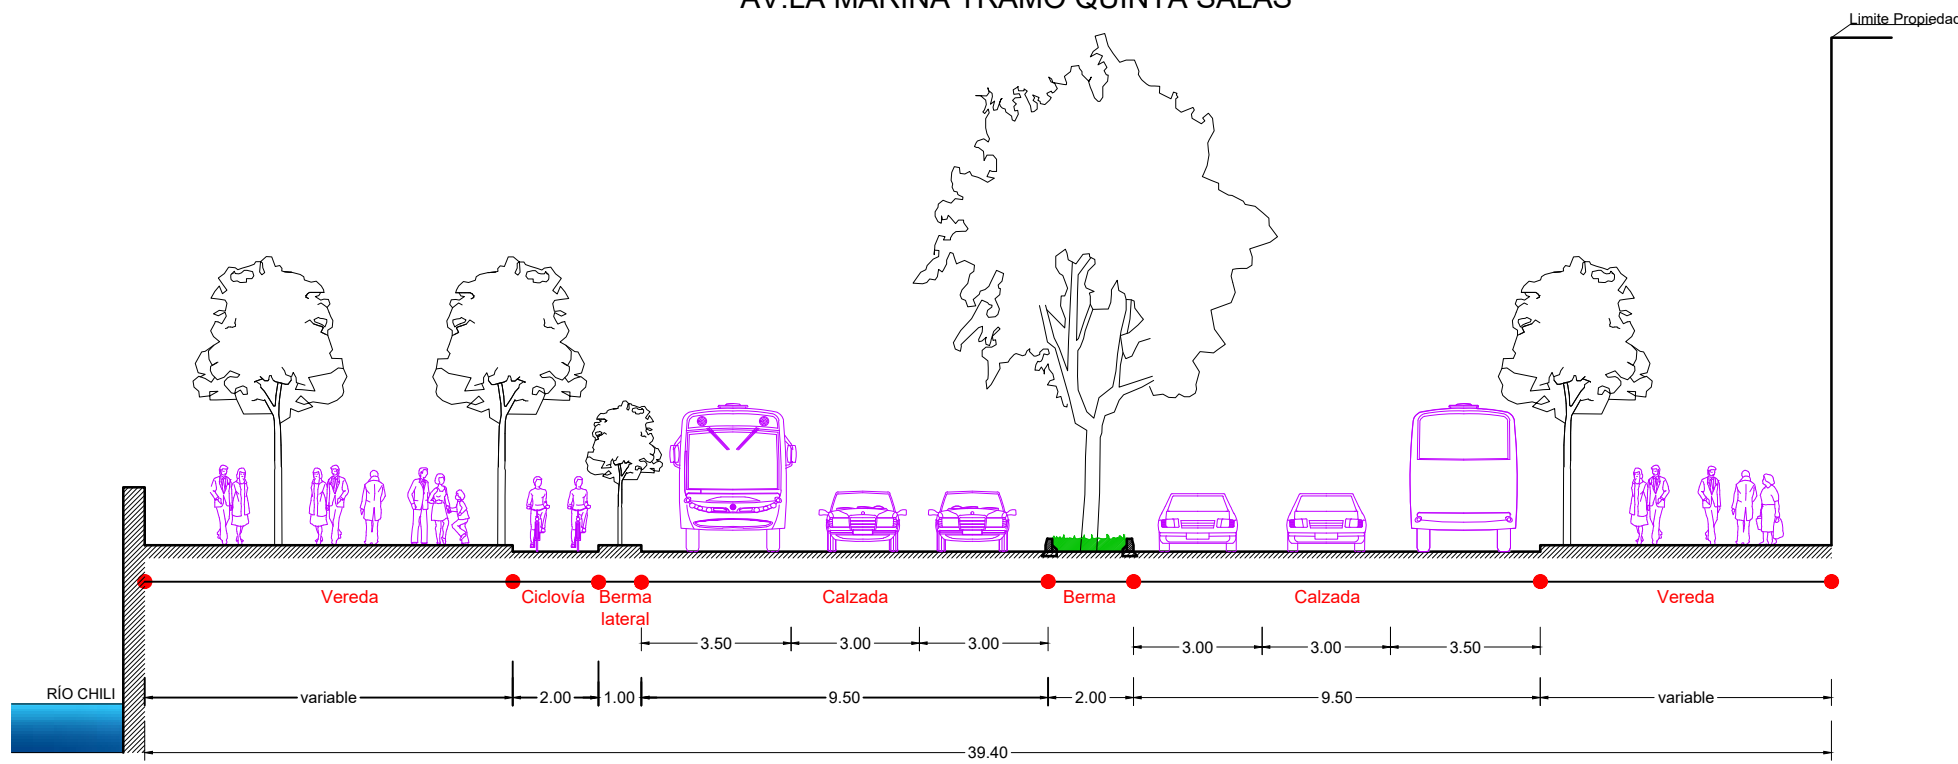


SECCIÓN VÍAL 8-8: VIA ARTERIAL
TRAMO CALLE PTE.GRAU

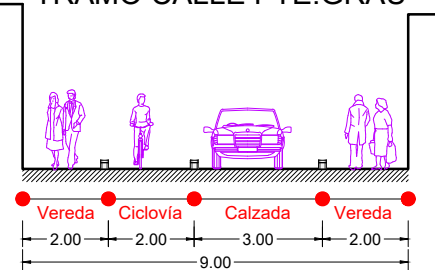


SECCIÓN VÍAL 9-9: VIA COLECTORA
TRAMO PTE. BAJO GRAU

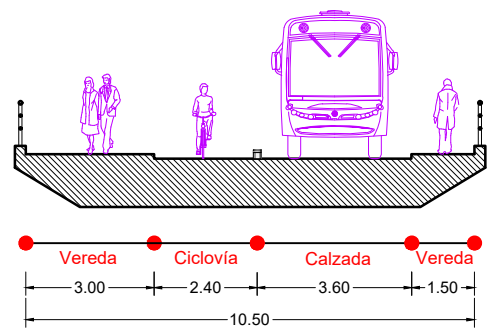


SECCIÓN VÍAL 10-10:
PUENTE DE FIERRO
VÍA PEATONAL COMPARTIDA 2

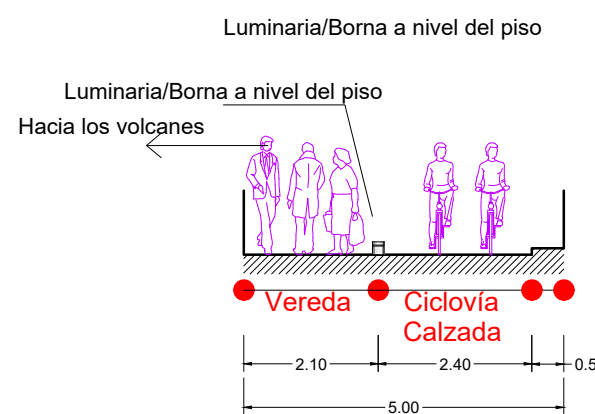


SECCIÓN VÍAL 11-11: ANILLO VIAL
AV.LA MARINA TRAMO PTE GRAU - PTE BOLOGNESI
PROPUESTA A LARGO PLAZO

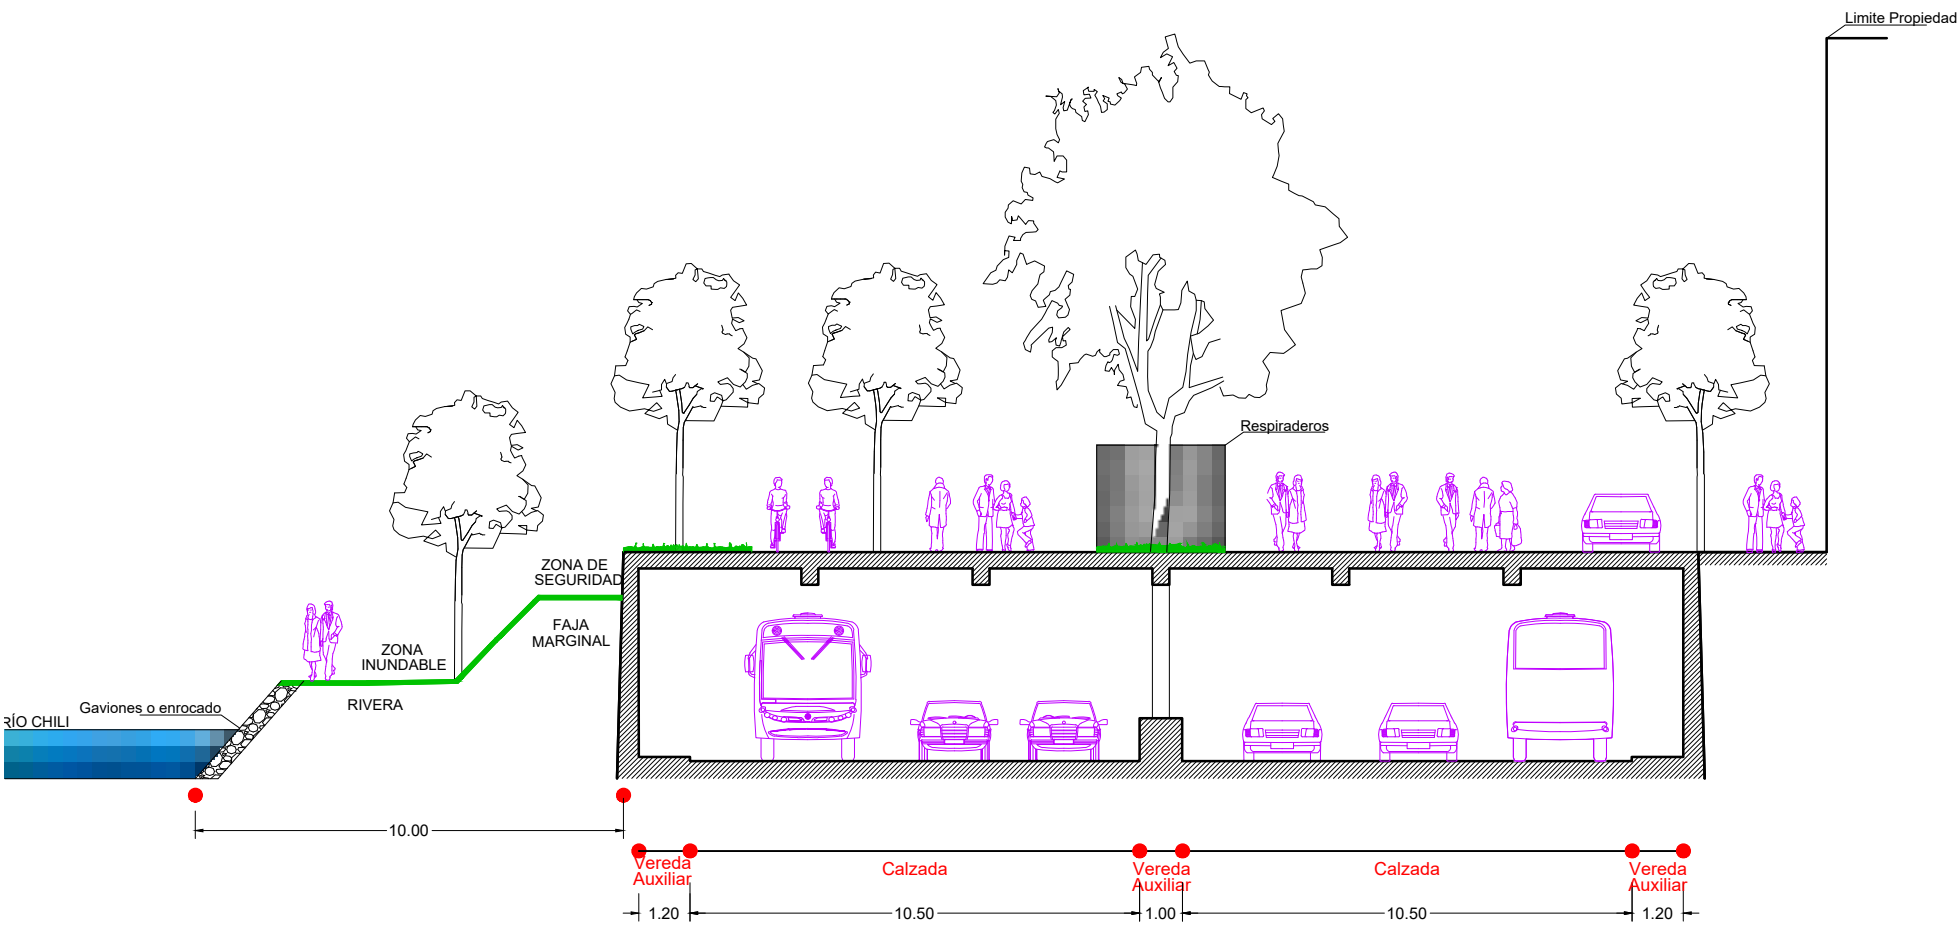

SECCIÓN VÍAL 12-12: ANILLO VIAL
AV.LA MARINA TRAMO PEDRO P.DÍAZ

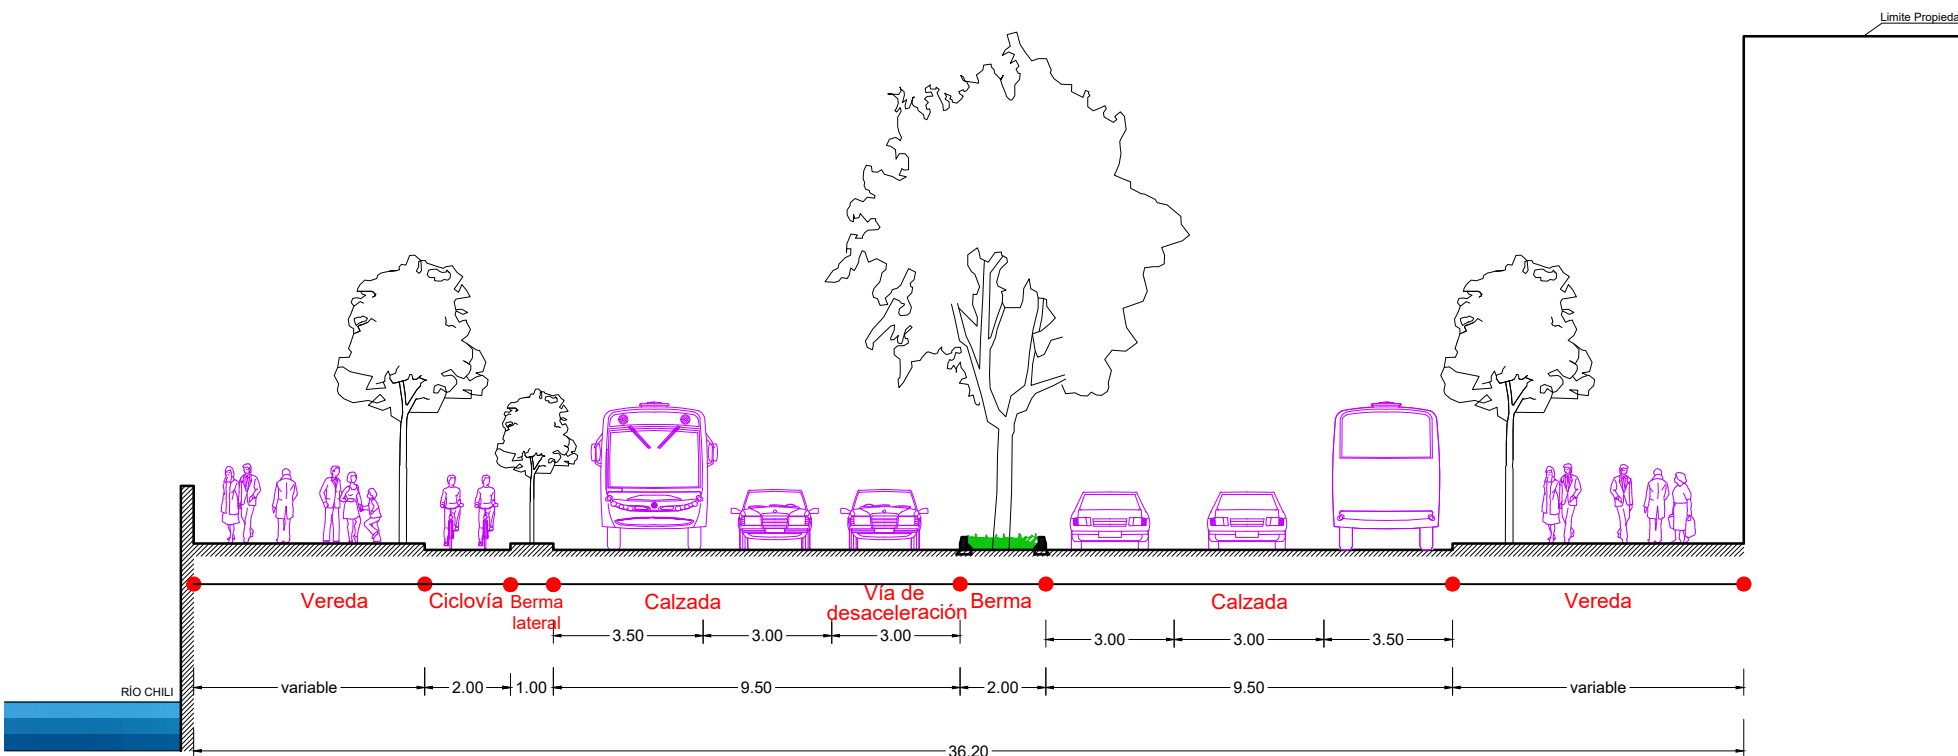

SECCIÓN VÍAL 13-13: ANILLO VIAL
AV.LA MARINA TRAMO PLAZA VEA

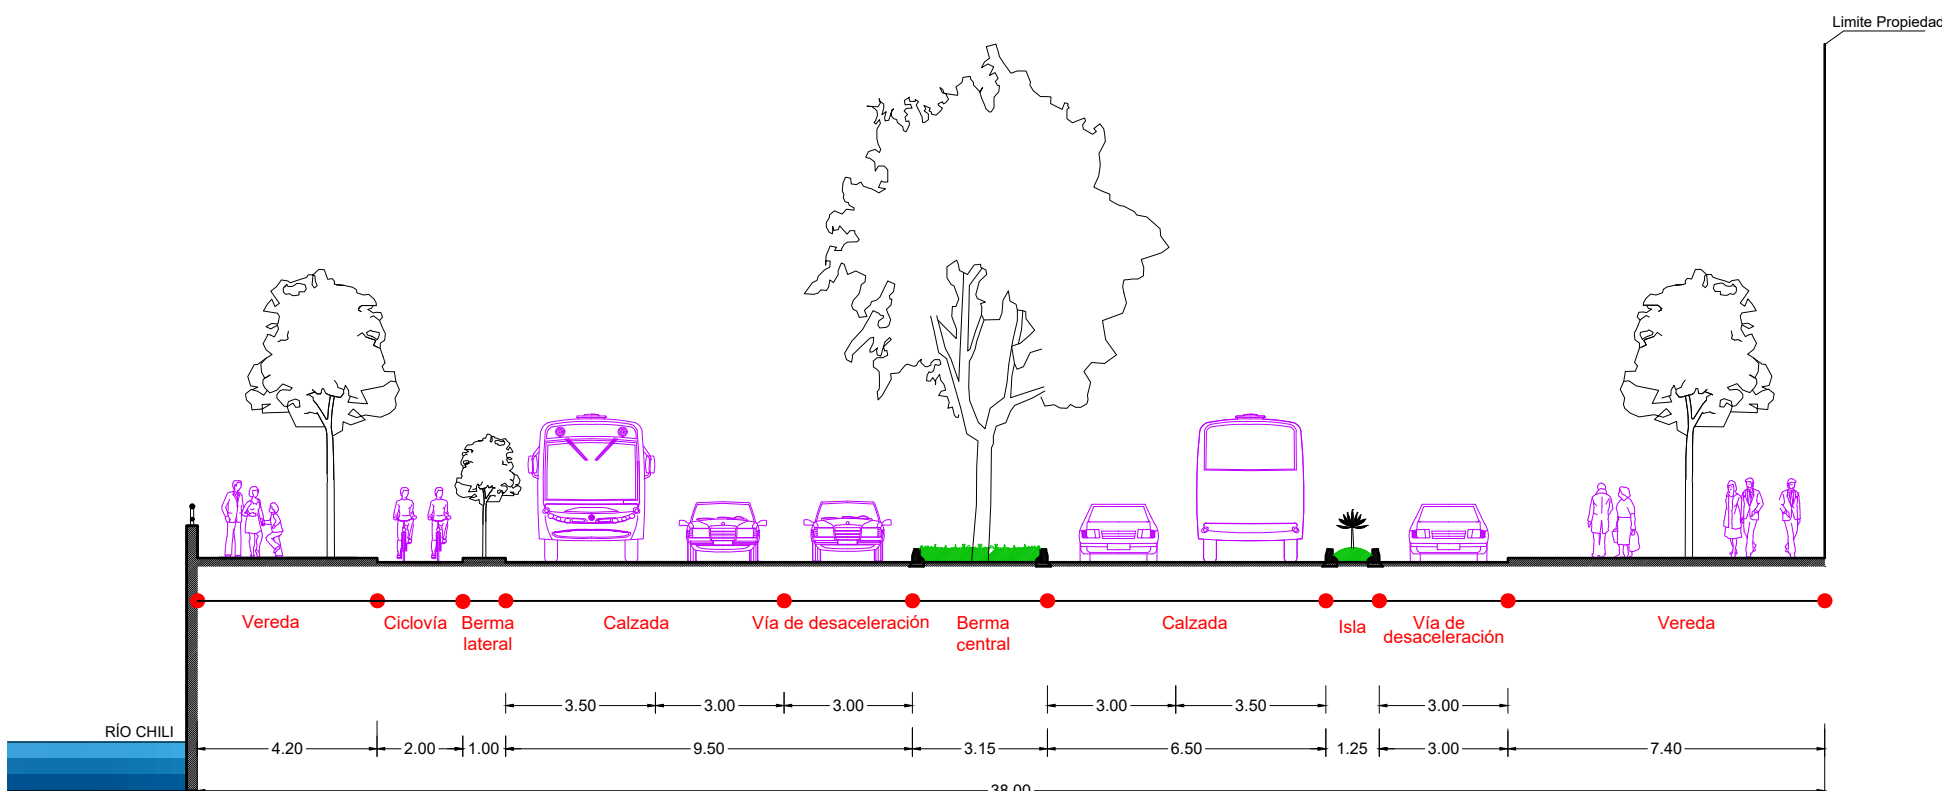

MUNICIPALIDAD PROVINCIAL
DE AREQUIPA

IMPLA
Instituto Municipal
de Planeamiento



GERENCIA DEL CENTRO HISTÓRICO
Y ZONA MONUMENTAL
ÁREA DE PLANIFICACIÓN
Y GESTIÓN URBANA



AECID
AGENCIA ESPAÑOLA
DE COOPERACIÓN INTERNACIONAL
PARA EL DESARROLLO

Plan Maestro del Centro
Histórico de Arequipa y
Zona de Amortiguamiento
PlaMCha
2025-2035
PF.05

PLANO

PROPUESTA VIAL
SECCIONES VIALES 2

ESC 1/4 500 NOVIEMBRE 2025 PSAD 56

MUNICIPALIDAD PROVINCIAL DE AREQUIPA

Alcalde
Ing. VICTOR HUGO RIVERA CHÁVEZ

IMPLA
Gerente General
Arq. PATRICIA MUÑOZ MEDINA

GERENCIA DEL CENTRO HISTÓRICO Y
ZONA MONUMENTAL

Gerente
Arq. GABRIEL RAMIRO DAMIANI LAZO

Coordinador Técnico General
Arq. JULIO C. ASPILCUETA BARBACHÁN

Equipo Técnico
Arq. Nancy Benavente Valcárcel
Arq. Yrma Daniela Villalba Linares
Arq. Candy Vanessa Año Urquiza
B.Arq. Rodrigo Arrieta Buscaglia
Abog. Juana Janina Tiznado Yana