



MUNICIPALIDAD PROVINCIAL
DE AREQUIPA

IMPLA
Instituto Municipal
de Planeamiento




GERENCIA DEL CENTRO HISTÓRICO
Y ZONA MONUMENTAL
ÁREA DE PLANIFICACIÓN
Y GESTIÓN URBANA




AECID
AGENCIA ESPAÑOLA
DE COOPERACIÓN INTERNACIONAL
PARA EL DESARROLLO


SECCIÓN VÍAL 14-14: ANILLO VIAL
AV.LA MARINA TRAMO 28 DE JULIO

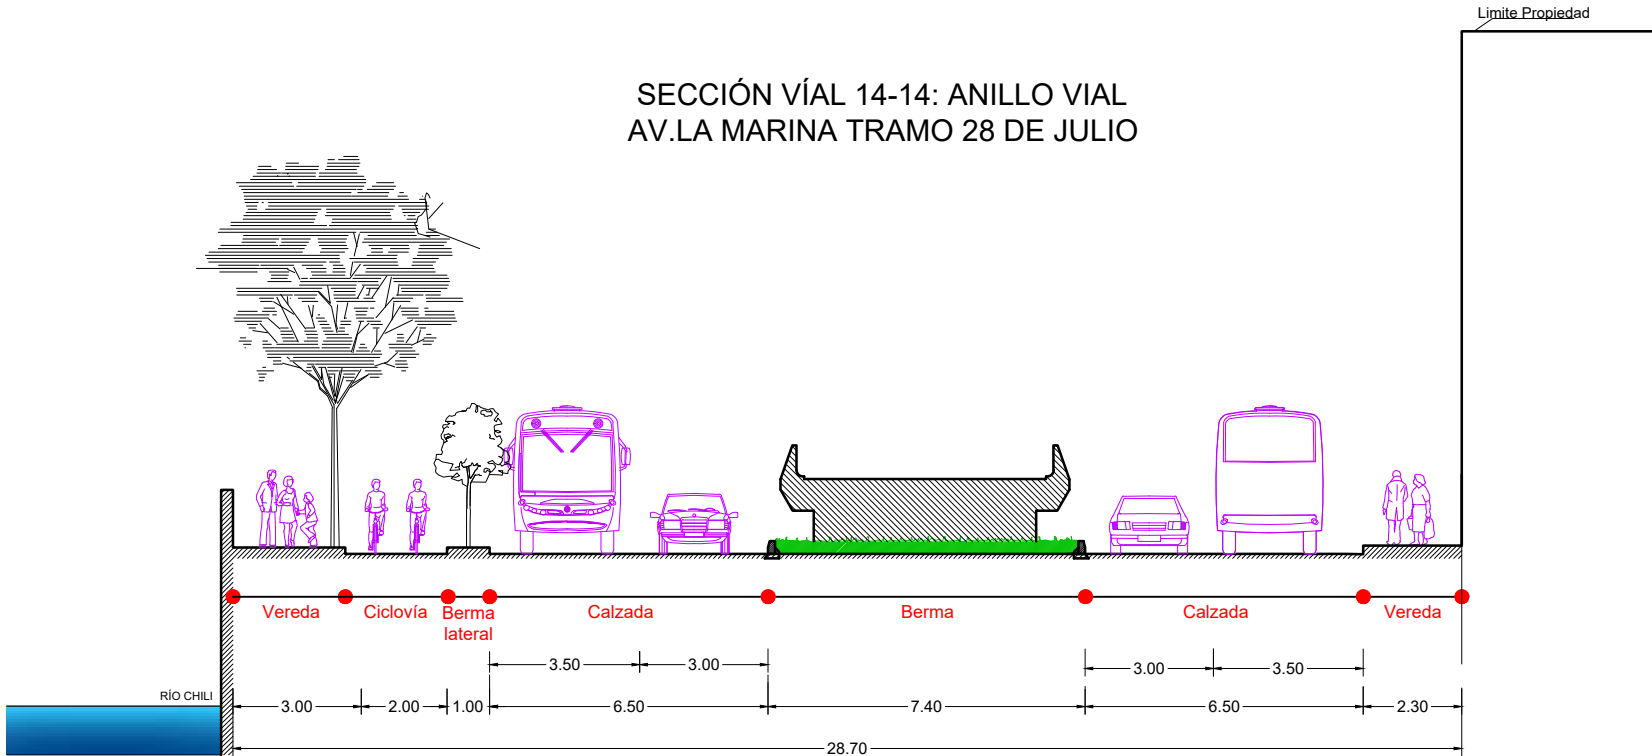


SECCIÓN VÍAL 15-15: ANILLO VIAL
AV.LA MARINA TRAMO CONSUELO

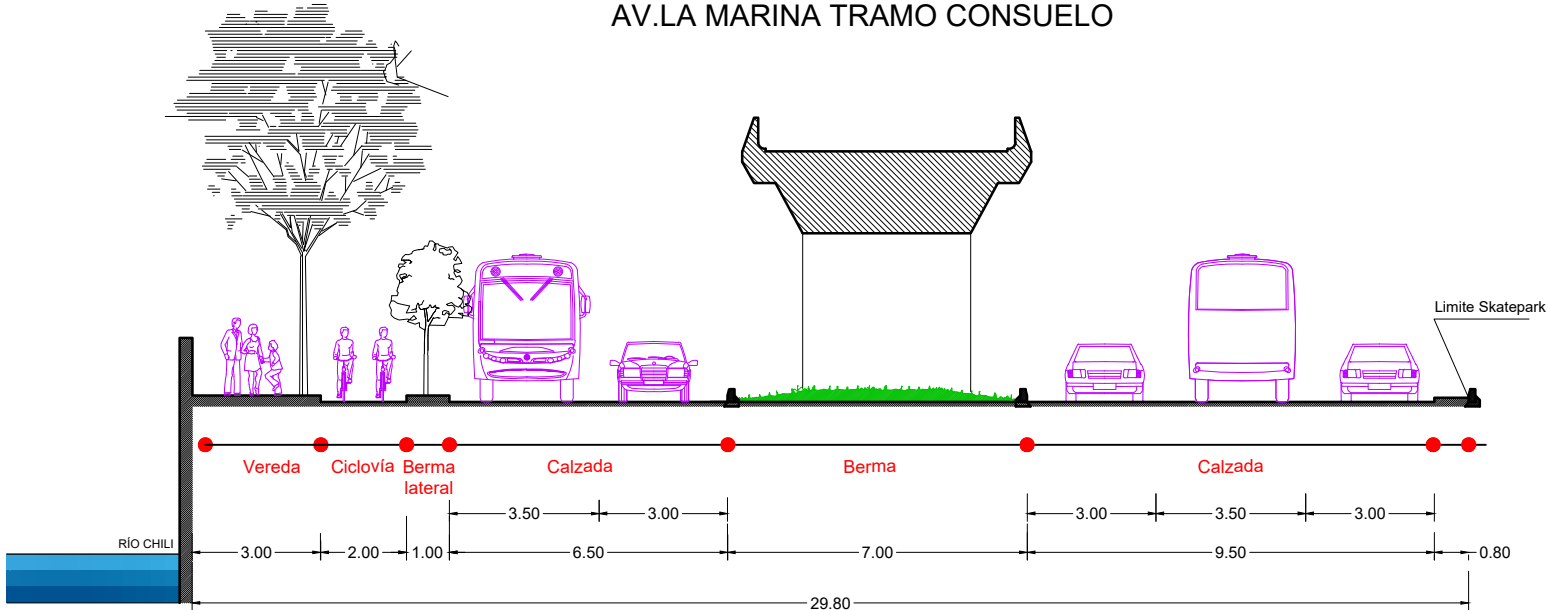


SECCIÓN VÍAL 16-16: ANILLO VIAL
AV.LA MARINA TRAMO PTE SAN MARTÍN.

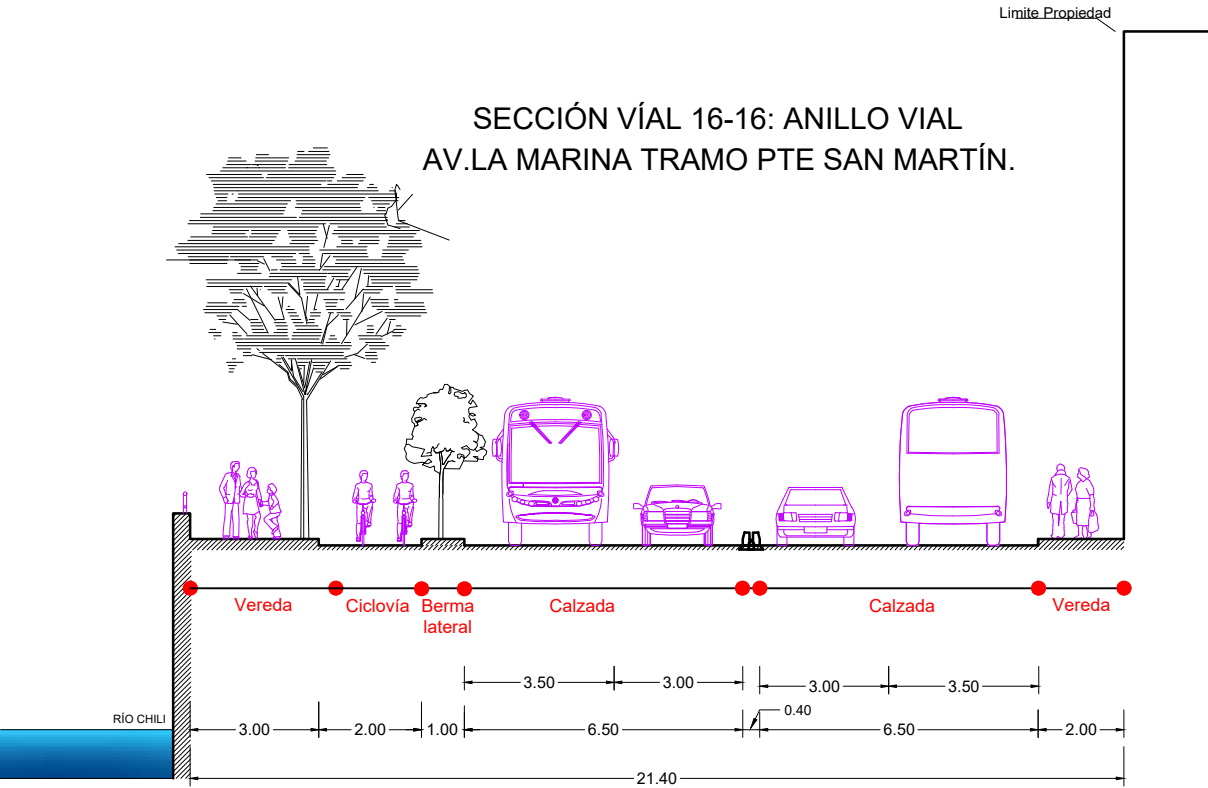


SECCIÓN VÍAL 17-17: VIA ARTERIAL
GOYENECHÉ - AV.JORGE CHÁVEZ
SECCIÓN 1

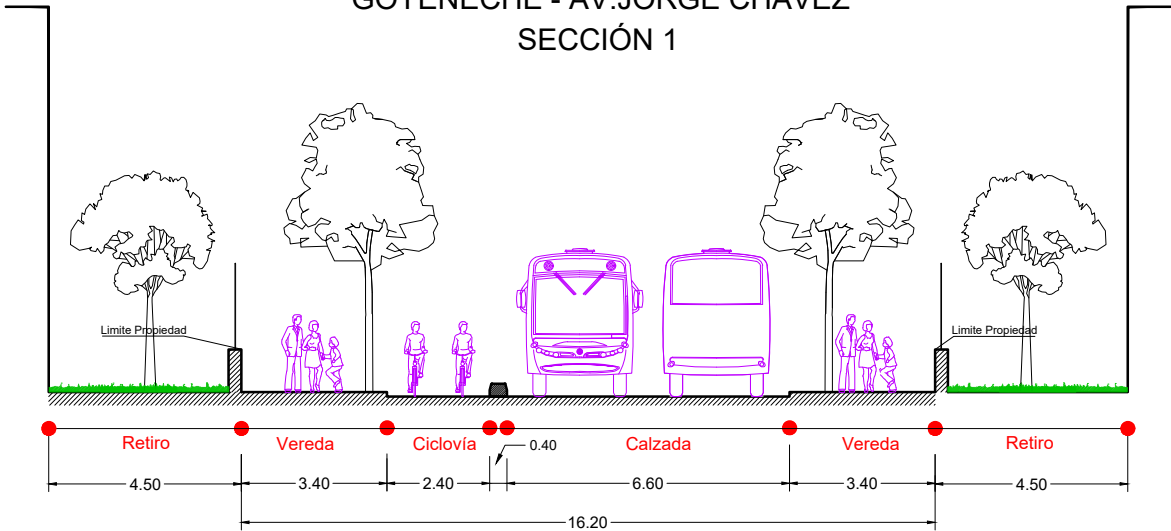

SECCIÓN VÍAL 18-18: VIA ARTERIAL
GOYENECHÉ - AV.JORGE CHÁVEZ
SECCIÓN 2

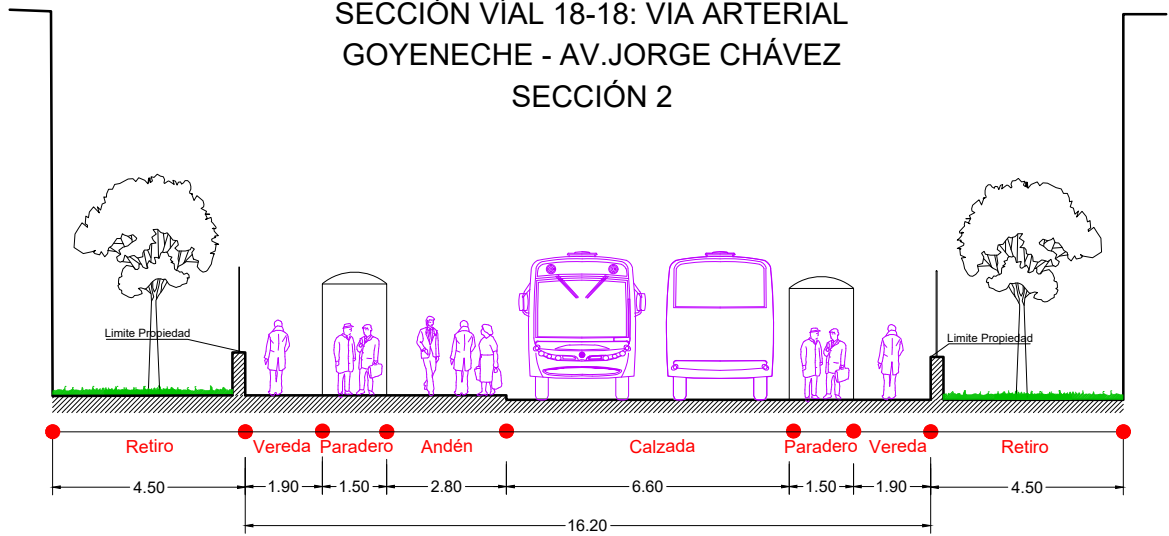

SECCIÓN VÍAL 19-19: ANILLO VIAL
AV.PROGRESO
SECCIÓN TÍPICA

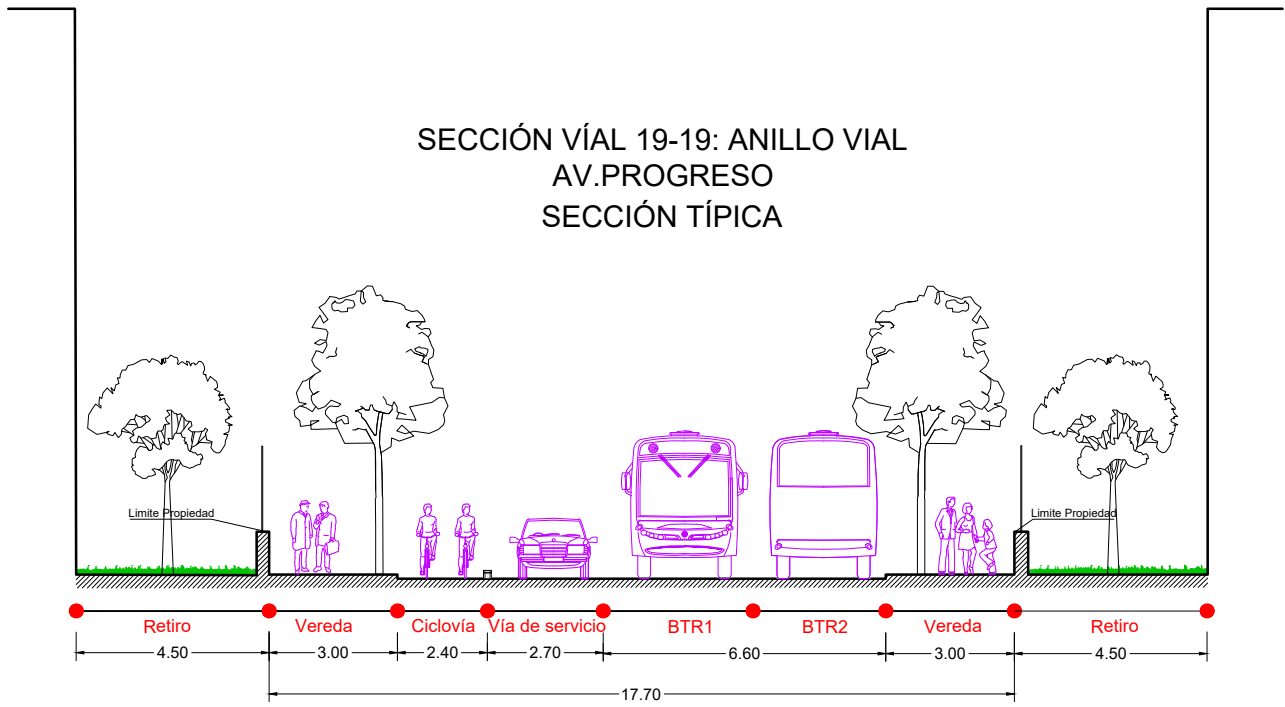

Plan Maestro del Centro
Histórico de Arequipa y
Zona de Amortiguamiento
PlaMCha
2025-2035
PF.06

PLANO
PROPUESTA VIAL
SECCIONES VIALES 3

ESC 1/4 500 NOVIEMBRE 2025 PSAD 56

MUNICIPALIDAD PROVINCIAL DE AREQUIPA

Alcalde
Ing. VICTOR HUGO RIVERA CHÁVEZ

IMPLA
Gerente General
Arq. PATRICIA MUÑOZ MEDINA

GERENCIA DEL CENTRO HISTÓRICO Y
ZONA MONUMENTAL

Gerente
Arq. GABRIEL RAMIRO DAMIANI LAZO

Coordinador Técnico General
Arq. JULIO C. ASPILCUETA BARBACHÁN

Equipo Técnico
Arq. Nancy Benavente Valcárcel
Arq. Yrma Daniela Villalba Linares
Arq. Candy Vanessa Año Urquiza
B.Arq. Rodrigo Arrieta Buscaglia
Abog. Juana Janina Tiznado Yana