



MUNICIPALIDAD PROVINCIAL
DE AREQUIPA

IMPLA
Instituto Municipal
de Planeamiento




GERENCIA DEL CENTRO HISTÓRICO
Y ZONA MONUMENTAL
ÁREA DE PLANIFICACIÓN
Y GESTIÓN URBANA




AECID
AGENCIA ESPAÑOLA
DE COOPERACIÓN INTERNACIONAL
PARA EL DESARROLLO


SECCIÓN VÍAL 20-20: ANILLO VIAL
AV. PROGRESO
SECCIÓN ESTACIÓN DE BUSES

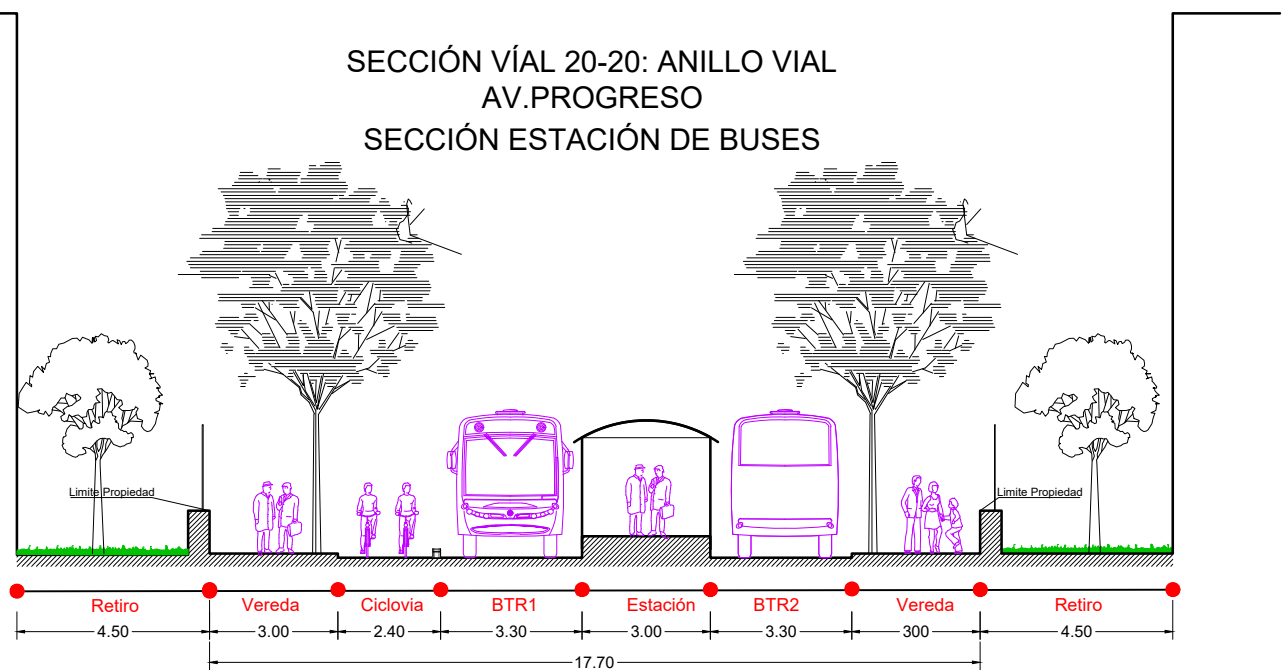


SECCIÓN VÍAL 21-21:
VIA LOCAL PRINCIPAL
AV. ZAMÁCOLA

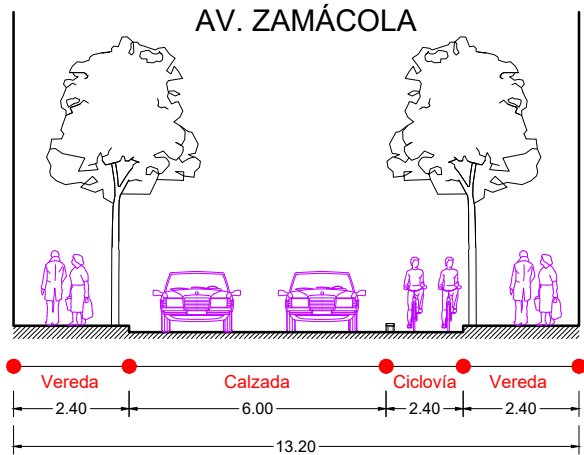


SECCIÓN VÍAL 22-22:
VIA LOCAL PRINCIPAL
AV. EMMEL

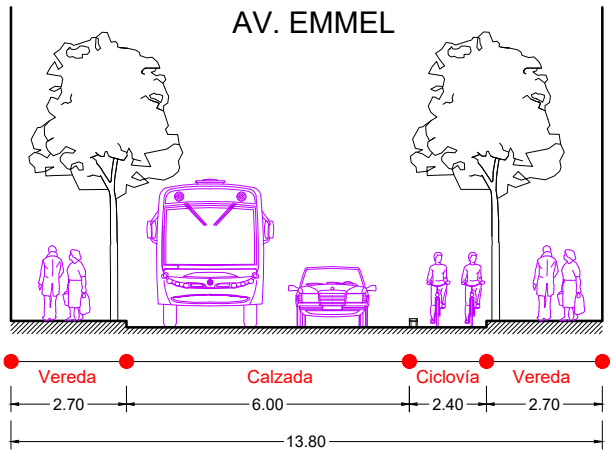


SECCIÓN VÍAL 23-23: VIA LOCAL
SECCIÓN VIAL TÍPICA 1
VÍA PEATONAL

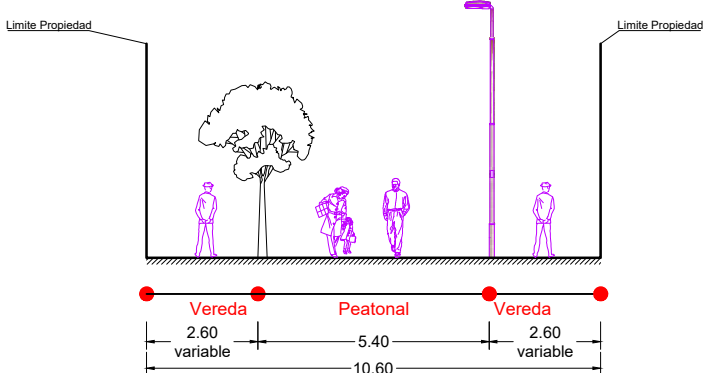


SECCIÓN VÍAL 24-24: VIA LOCAL
SECCIÓN VIAL TÍPICA 2
VÍA PEATONAL COMPARTIDA 2

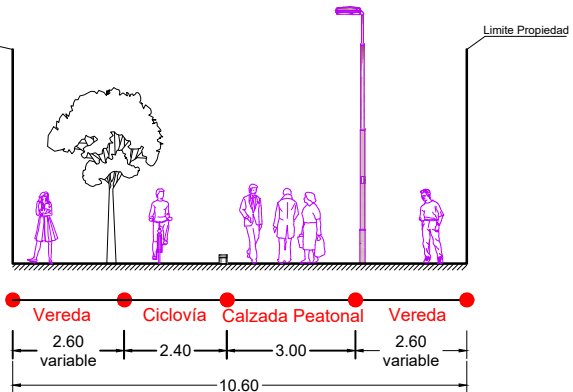


SECCIÓN VÍAL 25-25: VIA LOCAL
SECCIÓN VIAL TÍPICA 3
VÍA VEHICULAR

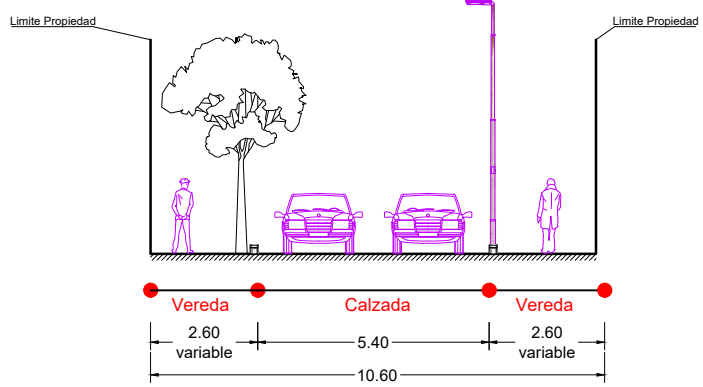


SECCIÓN VÍAL 26-26: VIA LOCAL
VÍA COMPARTIDA 1
(CON CICLOVÍA)

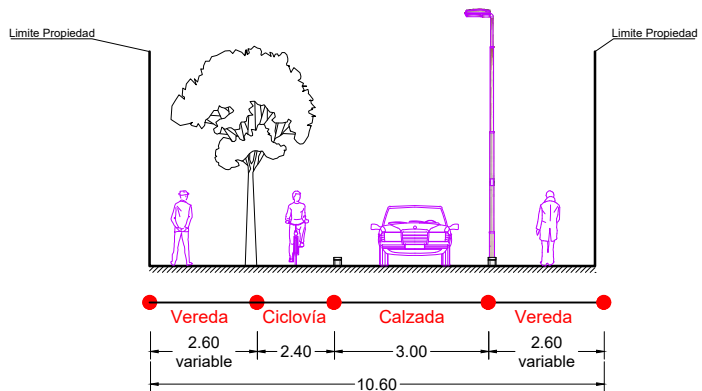


SECCIÓN VÍAL 27-27:
VIA LOCAL PRINCIPAL
JERUSALÉN

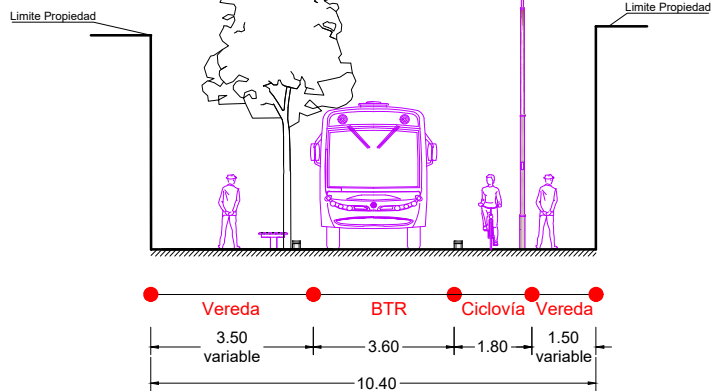


SECCIÓN VÍAL 28-28:
VIA LOCAL PRINCIPAL
SAN JUAN DE DIOS

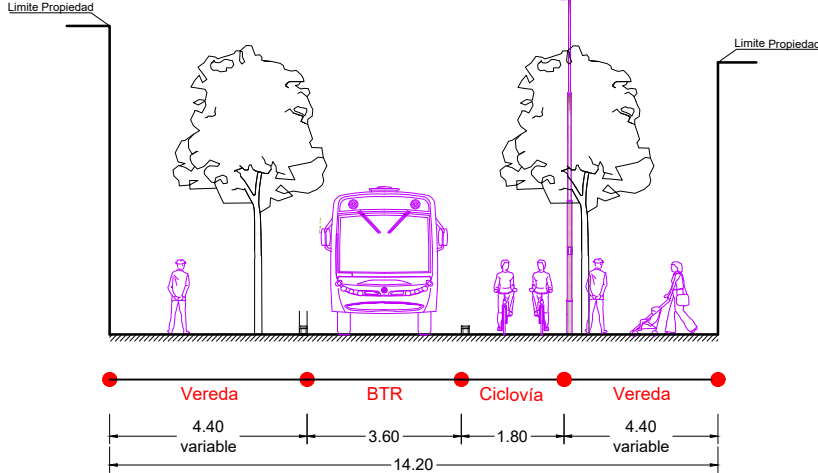


SECCIÓN VÍAL 29-29:
ZELA PRIMERA CUADRA

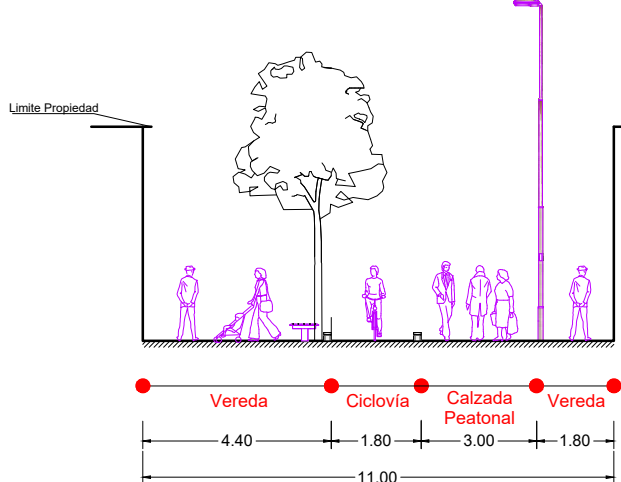

SECCIÓN VÍAL 30-30:
ZELA SEGUNDA CUADRA

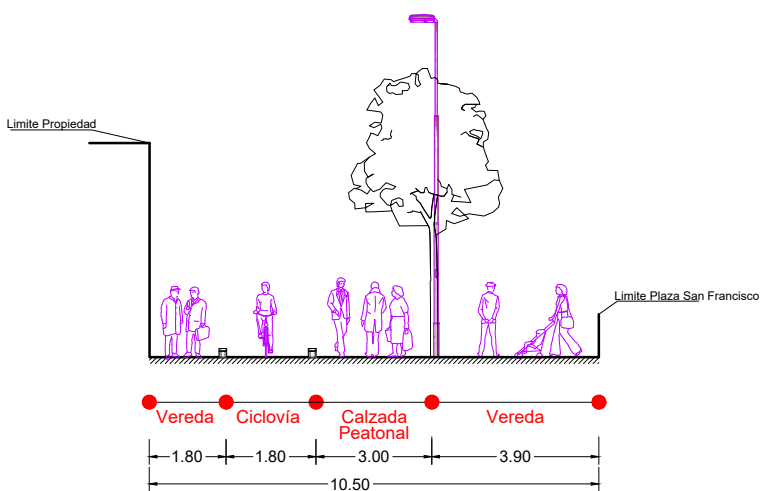

SECCIÓN VÍAL 31-31: VIA LOCAL PRINCIPAL
AV. SIGLO XX

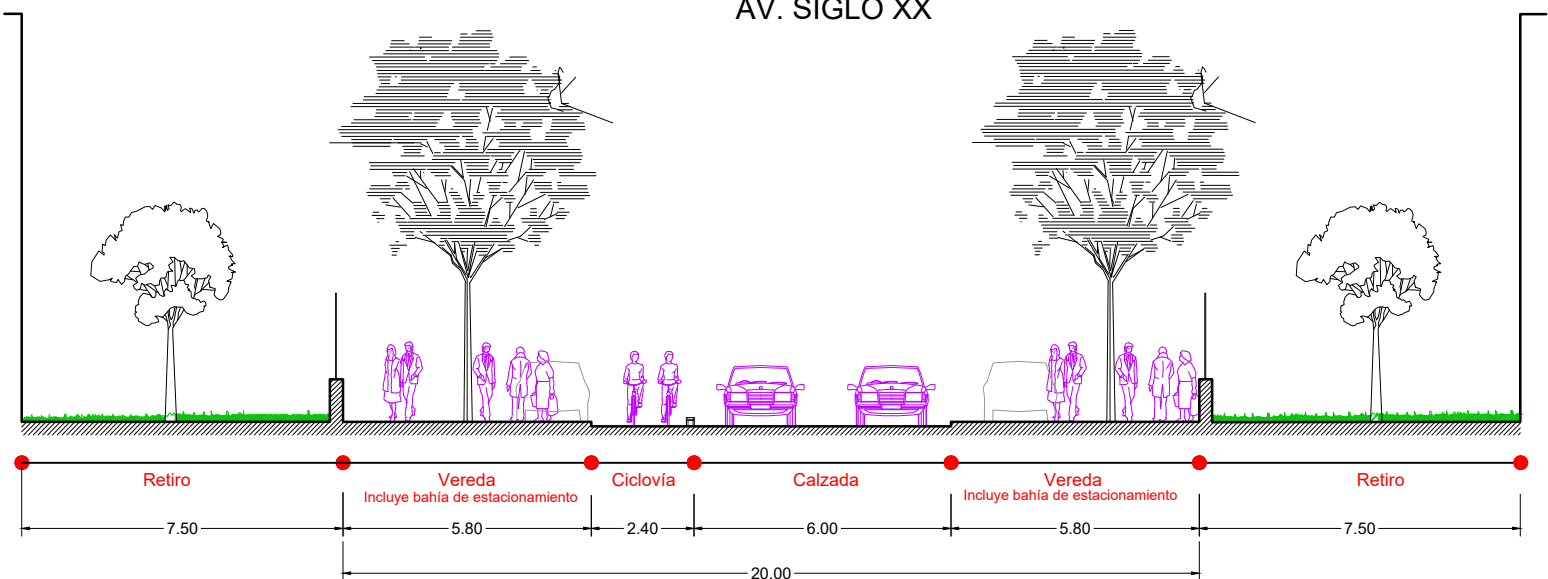

**Plan Maestro del Centro
Histórico de Arequipa y
Zona de Amortiguamiento
PlaMCha
2025-2035
PF.07**

PLANO

**PROPUESTA VIAL
SECCIONES VIALES 4**

ESC 1/4 500 NOVIEMBRE 2025 PSAD 56

MUNICIPALIDAD PROVINCIAL DE AREQUIPA

Alcalde
Ing. VICTOR HUGO RIVERA CHÁVEZ

IMPLA
Gerente General
Arq. PATRICIA MUÑOZ MEDINA

GERENCIA DEL CENTRO HISTÓRICO Y
ZONA MONUMENTAL

Gerente
Arq. GABRIEL RAMIRO DAMIANI LAZO

Coordinador Técnico General
Arq. JULIO C. ASPILCUETA BARBACHÁN

Equipo Técnico
Arq. Nancy Benavente Valcárcel
Arq. Yrma Daniela Villalba Linares
Arq. Candy Vanessa Año Urquiza
B.Arq. Rodrigo Arrieta Buscaglia
Abog. Juana Janina Tiznado Yana